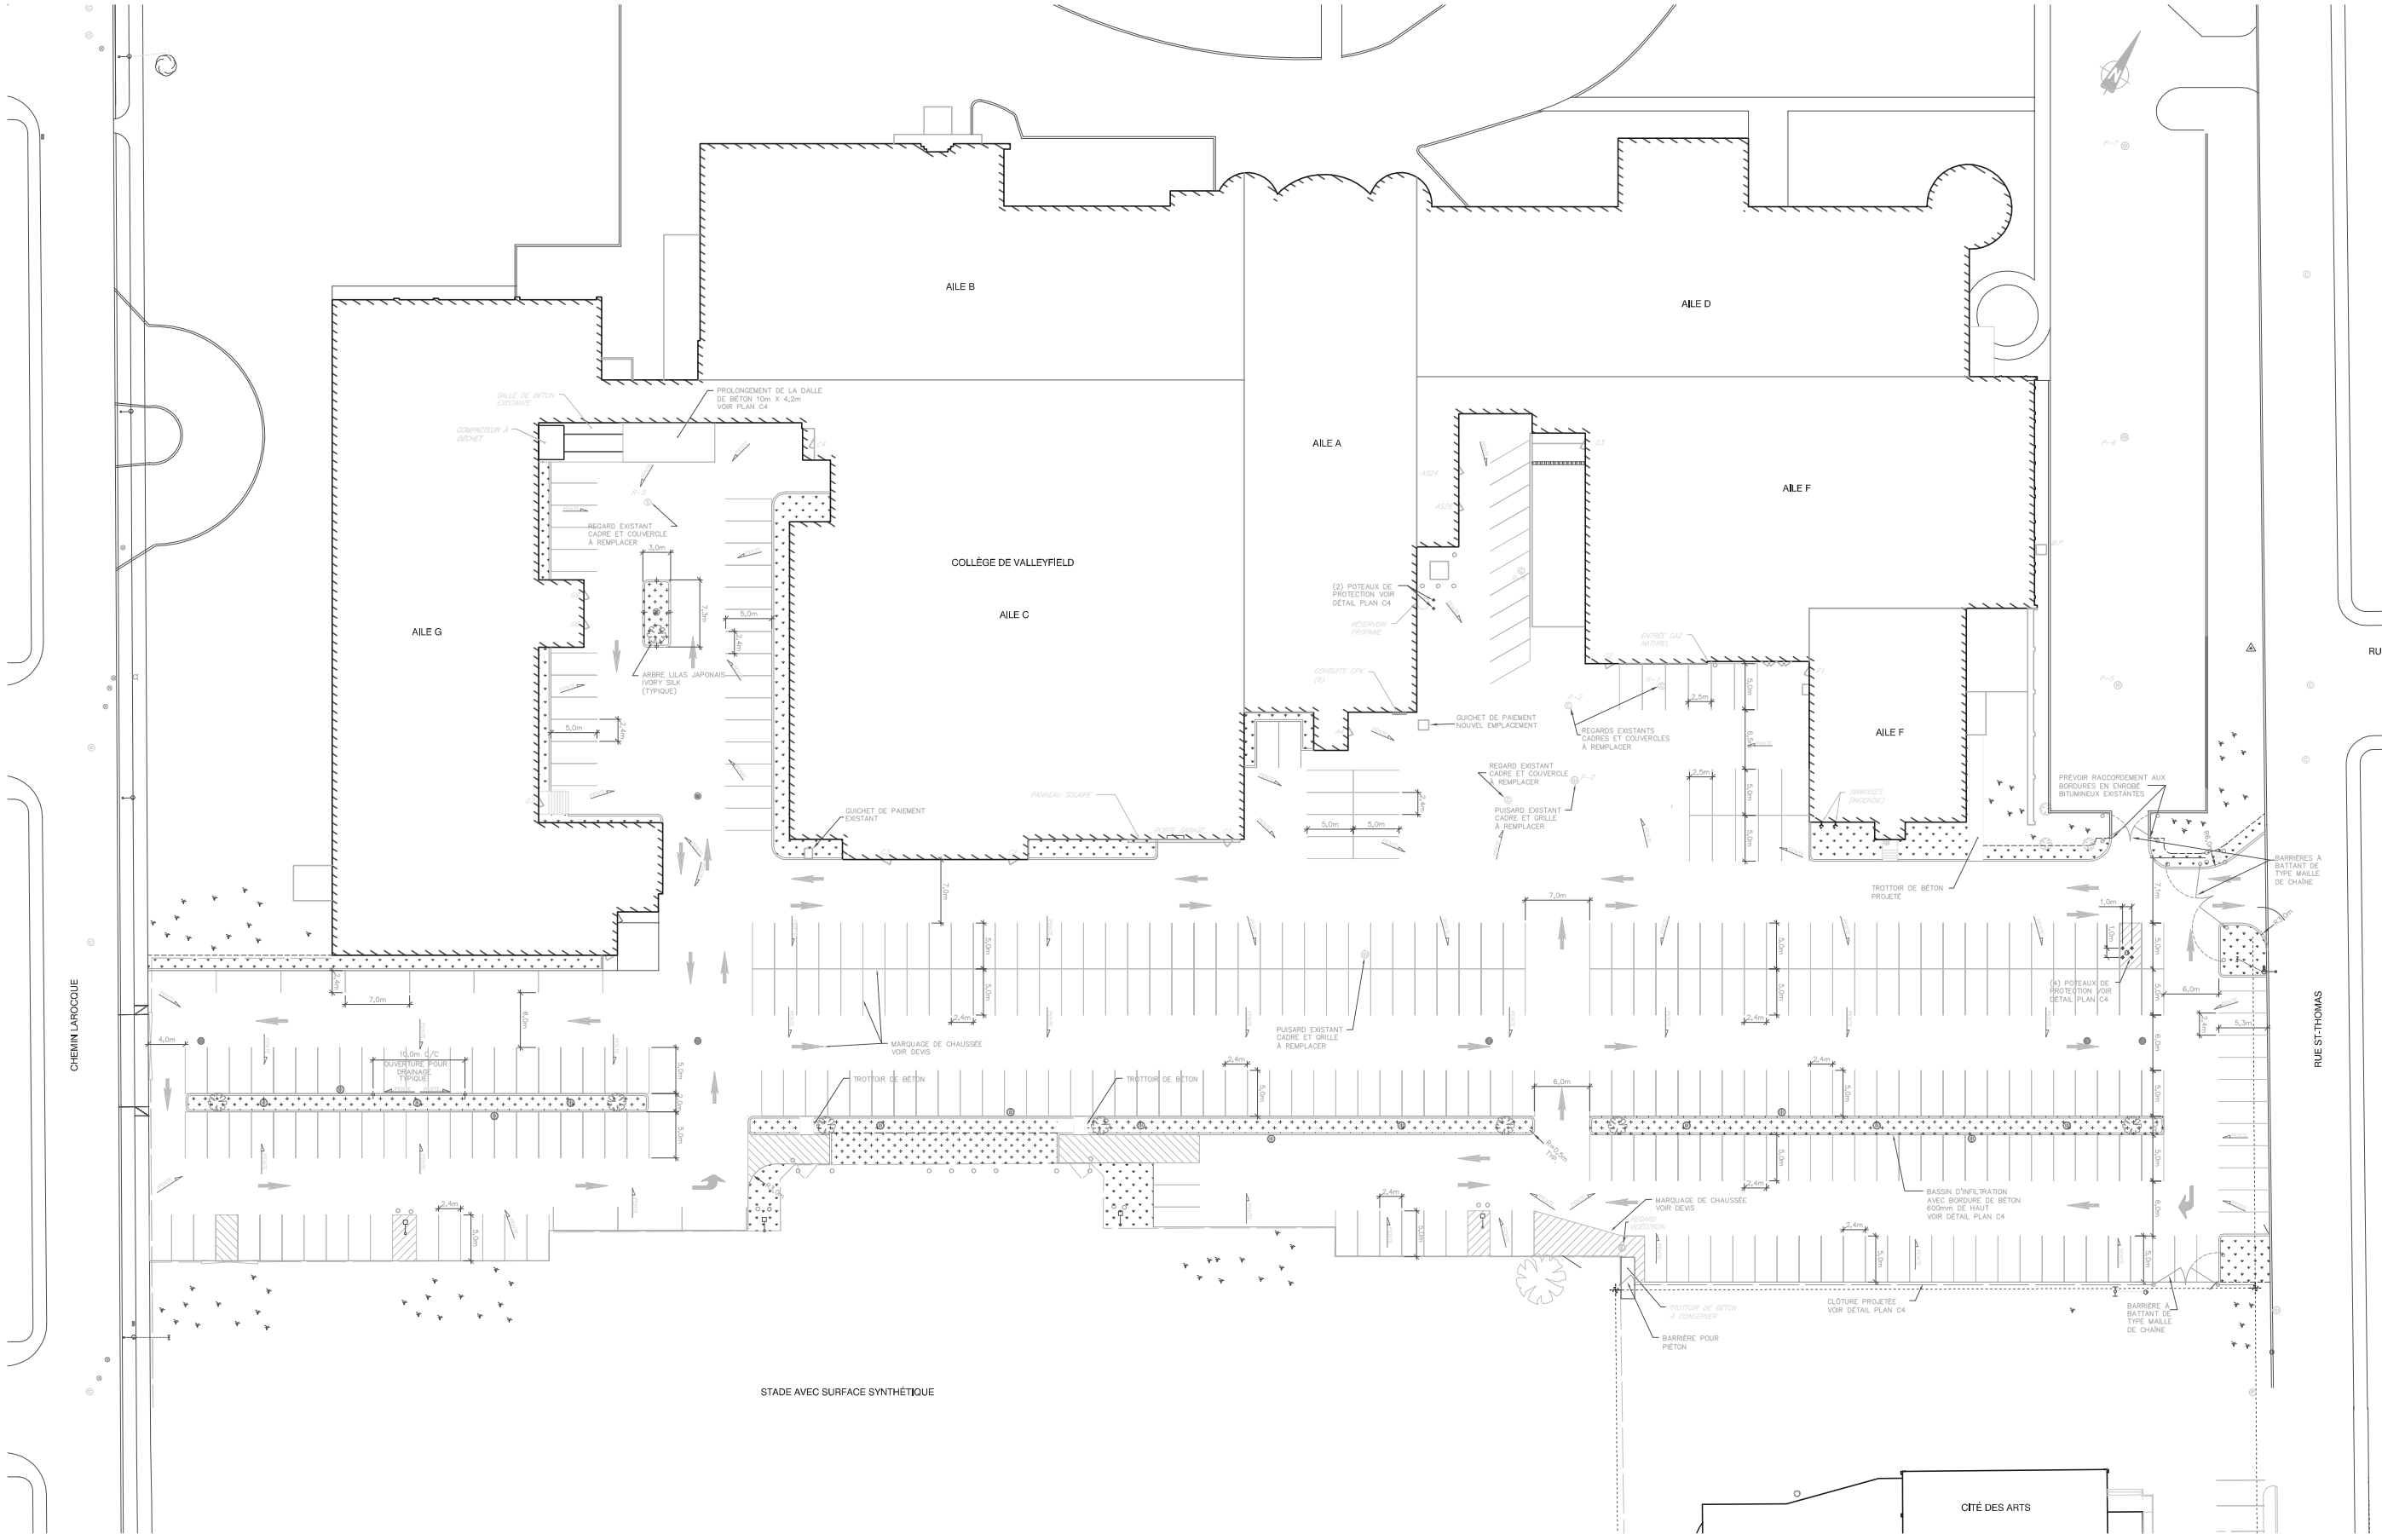

LEGENDE

	EXISTANT	PROPOSÉ
REGARD GAN/AM/RET/PLUV/E.P.		
PUISARD GRC/CAR/RECT		
REGARD PUISARD		
POSTE DE POMPAGE		
BORNE D'INCENDIE		
CHAMBRE DE VANNES		
VANNE		
RÉDUIT		
BOUCHON		
ENTRÉE DE SERVICE		
ÉGOUT SANITAIRE		
ÉGOUT SANITAIRE (PROFIL)		
ÉGOUT PLUVIAL		
ÉGOUT PLUVIAL (PROFIL)		
ÉGOUT UNITAIRE		
ÉGOUT UNITAIRE (PROFIL)		
CONDUITE DE RETOULEMENT		
CONDUITE DE RETOUL(REMP/PROP)		
CONDUITE EAU POTABLE (ADEQ/EC)		
COMBINE EAU POTABLE (NIDEQ) (PROF)		
DRAIN PERFORÉ		
FAVAGE		
GRAVIER		
TROTTOIR		
BORDURE		
CLÔTURE		
GLISSIÈRE		
FOSSÉ		
PONCEAU		
HAUT DE TALUS		
BAS DE TALUS		
HAIE		
LIGNE DE LOT		
LIGNE D'EMPRISE		
ÉLÉVATION TERRAIN		
GAZON		
PLANTATION AUX BASSINS D'INFILTRATIONS		
LAMPADAIRE		
SONDAGE/FORAGE (EN PLAN)		EN PROFIL
REPÈRES DE NIVELLEMENT		
STATION D'ARPENTAGE		
BORNE/TIGE DE FER		
POTEAU ÉLECTRIQUE		
POTEAU DE TÉLÉPHONE		
POTEAU DE TÉLÉPHONE AVEC TRANSFO.		
POTEAU ÉLECTRIQUE/TÉLÉPHONIQUE		
HAUBAN		
ÉLEC. ENFOUIE / REGARD / BU		
GAZ ENFOUI / REGARD		
TÉLÉPHONE ENFOUI / REGARD / BU		
CABLODISTRIBUTION ENFOUI / REGARD		

POUR SOUMISSION
NE PEUT SERVIR À LA CONSTRUCTION
2011-03-23

0	2011-03-23	ÉMIS POUR SOUMISSION	D.T.

Échelle de 1:250 à 1:500
Dessin: D.T.
Vérifié par: V.P.
Approuvé par: M.Q.
Date: 2011-03-23
Dessin no: CVDG-007-C3
Révision: 0
Description: IMPLANTATION TERRASSEMENT VOIRIE MARQUAGE

Collège de Valleyfield
L'HISTOIRE L'EXPÉRIENCE LE SUCCÈS

IMPLANTATION TERRASSEMENT, VOIRIE ET MARQUAGE

D.TRUDEL ing.	2011-03-14	C3
V.PETIT ing.j.	1 : 250M	C4
M. QUIRION	CVDG-007	0

CVDG-007-C3.dwg

0 6,25m 12,5m